


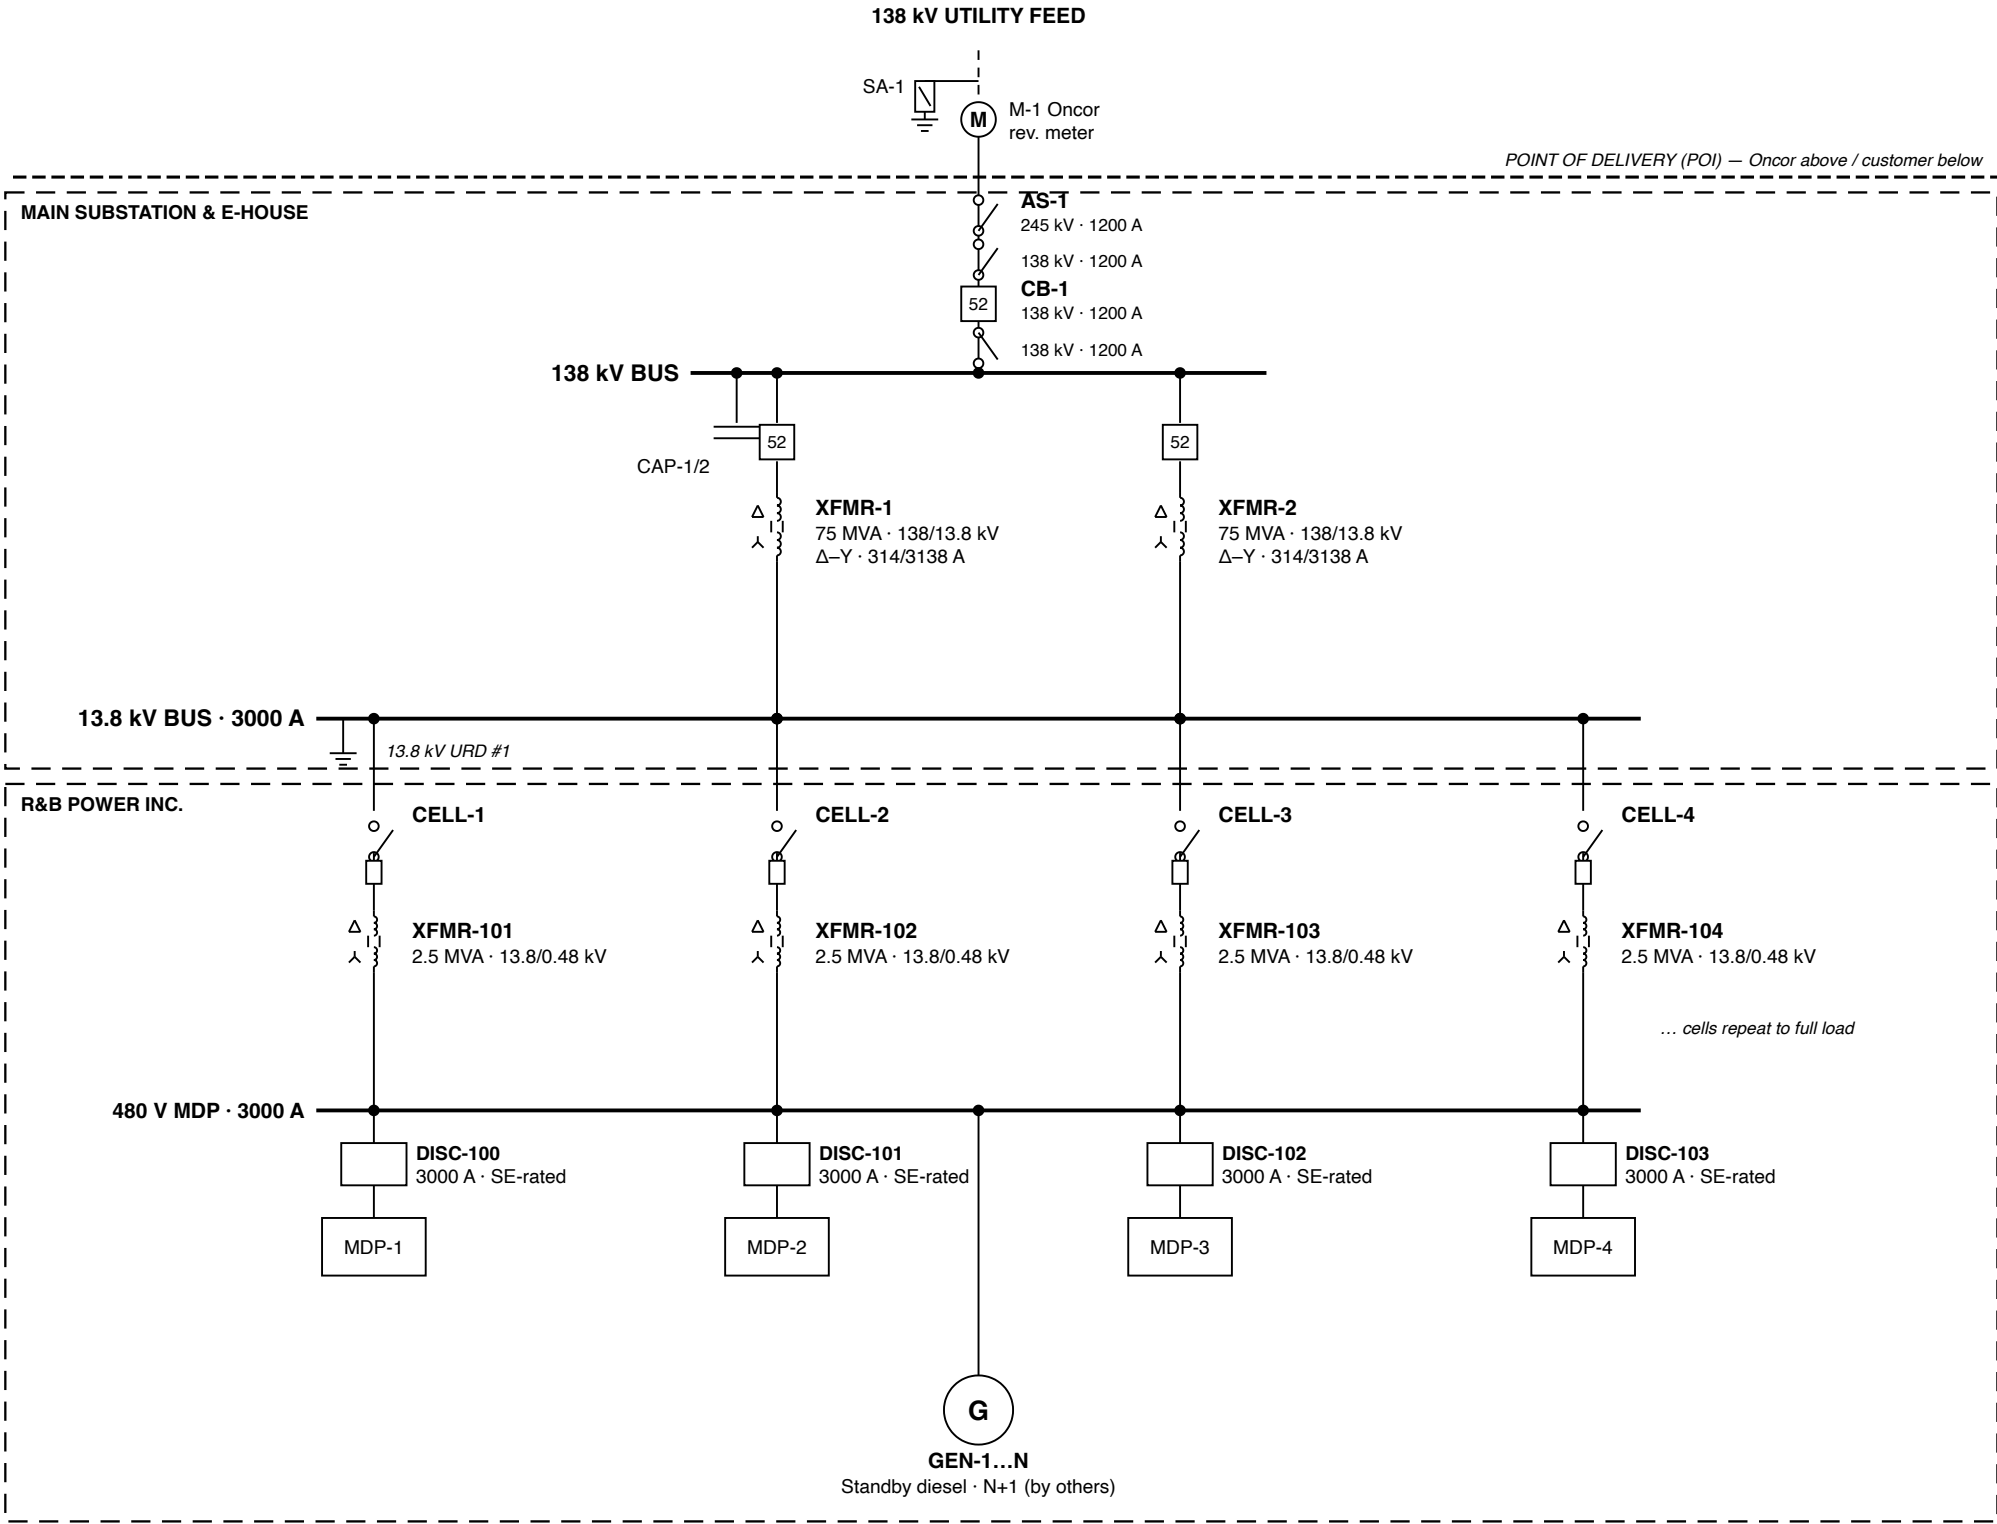

GENERAL NOTES

- Service: single 138 kV feed; Oncor revenue metering (xfmr-rated) & arresters above POI.
- Ultimate 60 MW (~62 MVA @ 0.97 pf), data center.
- 2 × 75 MVA (N-1 firm 75 MVA); dashed transformers = future phase.
- Single 138 kV feed; radial customer substation.
- %Z, tap range, kA, CT/PT & relays — by final design.

LEGEND

- Disconnect switch
- 52 Circuit breaker
- Power transformer (Δ-Y)
- Fuse
- Capacitor bank
- Generator
- Surge arrester
- Revenue meter
- Connection (junction)

REV 1 · Issued for Interconnection Study · RBP · 2026-06-08

ELECTRICAL ONE-LINE DIAGRAM

Single-Feed Test — 60 MW
TX

Customer: NTNSM, LLC

R&B Power Inc.
Dwg RB-SF-E-001 · Rev 1
Scale: AS SHOWN · Sheet 1 of 1
Study-stage · not for construction

TOTAL CONNECTED LOAD: 60 MW (~62 MVA @ 0.97 pf) · data center

Service: 138 kV feed · 795 kcmil ACSR · 2 × 75 MVA (N-1 firm 75) · per-feed 259 A